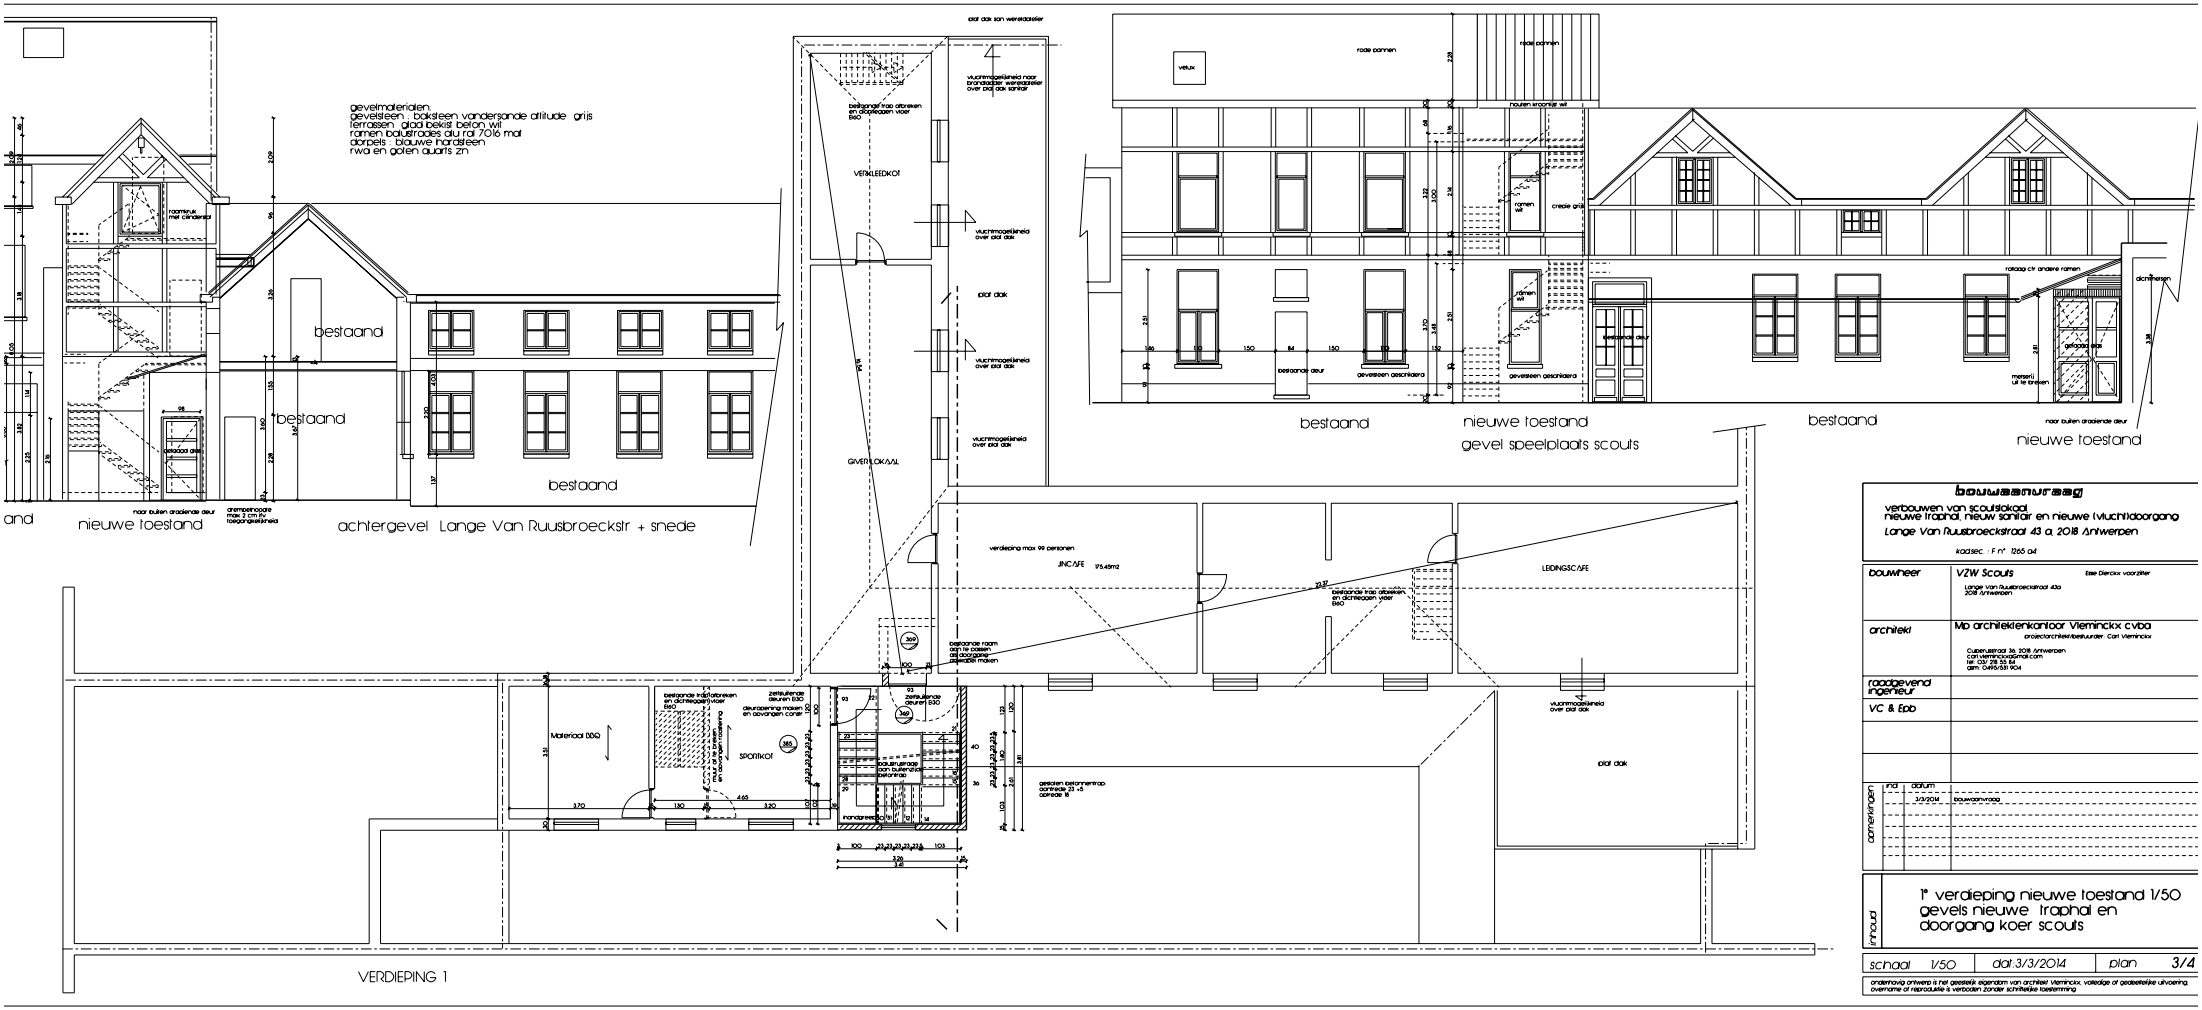

bouwaanvraag

verbouwen van scoutslokaal
nieuwe traphal, nieuw sanitair en nieuwe (vluchtdoorgang
Lange Van Ruusbroeckstraat 43 a, 2018 Antwerpen

kadasec : F nr° 1265 a4

bouwheer	VZW Scouts — Elsie Dierckx voorzitter Lange Van Ruusbroeckstraat 43a 2018 Antwerpen
architekt	Mb architektenkantoor Vlerninckx cvba projectarchitekt/bestuurder: Carl Vlerninckx Cuperusstraat 36, 2018 Antwerpen carl.vlerninckx@gmail.com tel: 03/ 218 55 54 gsm: 0495/531 904
raadgevend ingenieur	
VC & Epb	

opmerkingen	nr	datum	
		3/3/2014	bouwaanvraag

inhoud: 1° verdieping nieuwe toestand 1/50 gevels nieuwe traphal en doorgang koer scouts

schaal	1/50	dat:3/3/2014	plan	3/4

onderhavig ontwerp is het geestelijk eigendom van architekt Vlerninckx, volledige of gedeeltelijke uitvoering, overname of reproduktie is verboden zonder schriftelijke toestemming