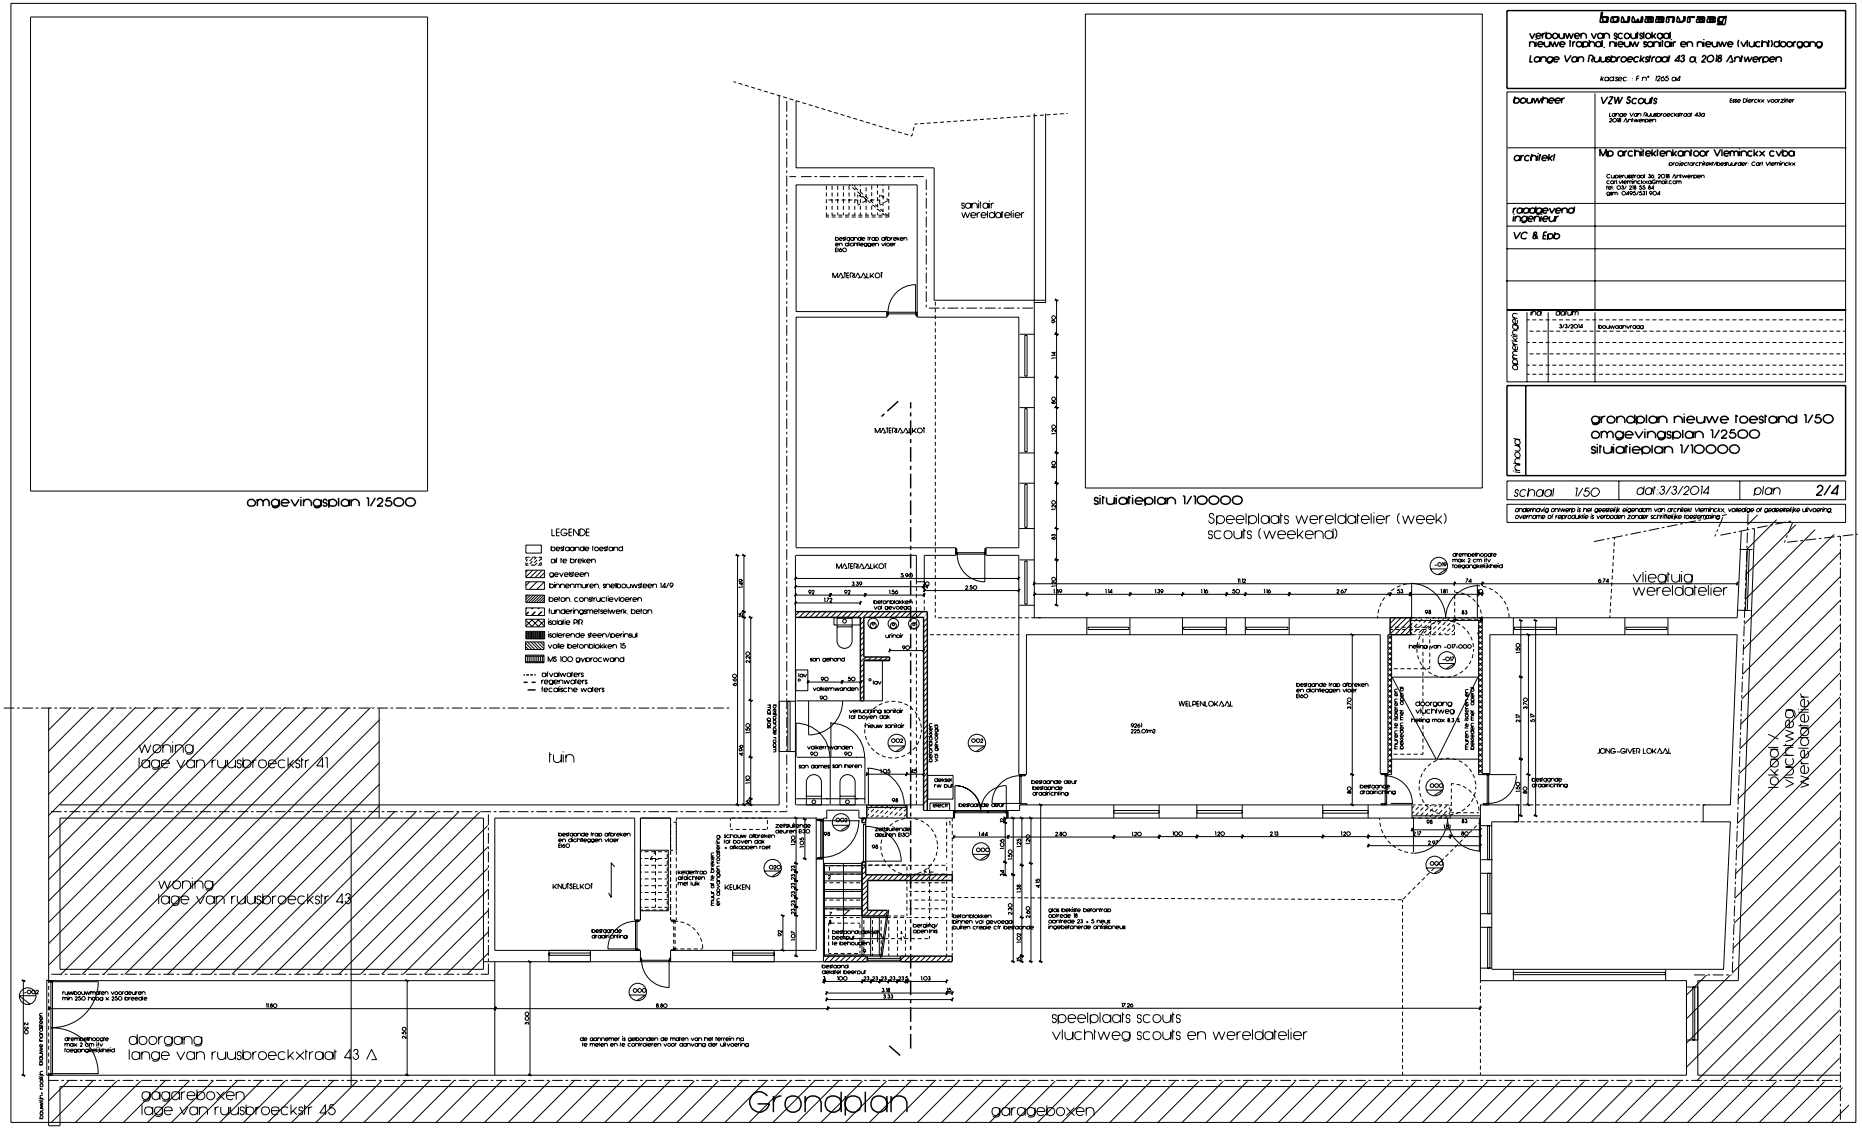

bouwaanvraag

verbouwen van scoutslokaal,
nieuwe traphal, nieuw sanitair en nieuwe (vlucht)doorgang
Lange Van Ruusbroeckstraat 43 a, 2018 Antwerpen

kadasec : F nr° 1265 d4

bouwheer	VZW Scouts — Ellse Dierckx voorzitter Lange Van Ruusbroeckstraat 43a 2018 Antwerpen
architekt	Mb architektenkantoor Vlemincks cvba ontwerparchitekt/bestuurder: Carl Vlemincks Cuperusstraat 36, 2018 Antwerpen carl.vlemincks@gmail.com tel: 03/ 218 33 67 gsm: 0495/531 904
raadgevend ingenieur	
VC & Epb	

opmerkingen

nr	datum	
	3/3/2014	bouwaanvraag

inhoud: grondplan nieuwe toestand 1/50
omgevingsplan 1/2500
situatieplan 1/10000

schaal	1/50	dat 3/3/2014	plan	2/4

ondertekend ontwerp is het geestelijk eigendom van architekt Vlemincks, volledige of gedeeltelijke uitvoering, overname of reproduktie is verboden zonder schriftelijke toestemming.